


TREE LEGEND

- A - EXISTING TREES TO REMAIN
B - PROPOSED OVERSTORY TREES, 2"-2 1/2" CAL., B&B
C - PROPOSED UNDERSTORY TREES, 8'-10' HT, B&B
D - PROPOSED EVERGREEN TREES, 6'-8' HT, B&B


FENCE DETAIL

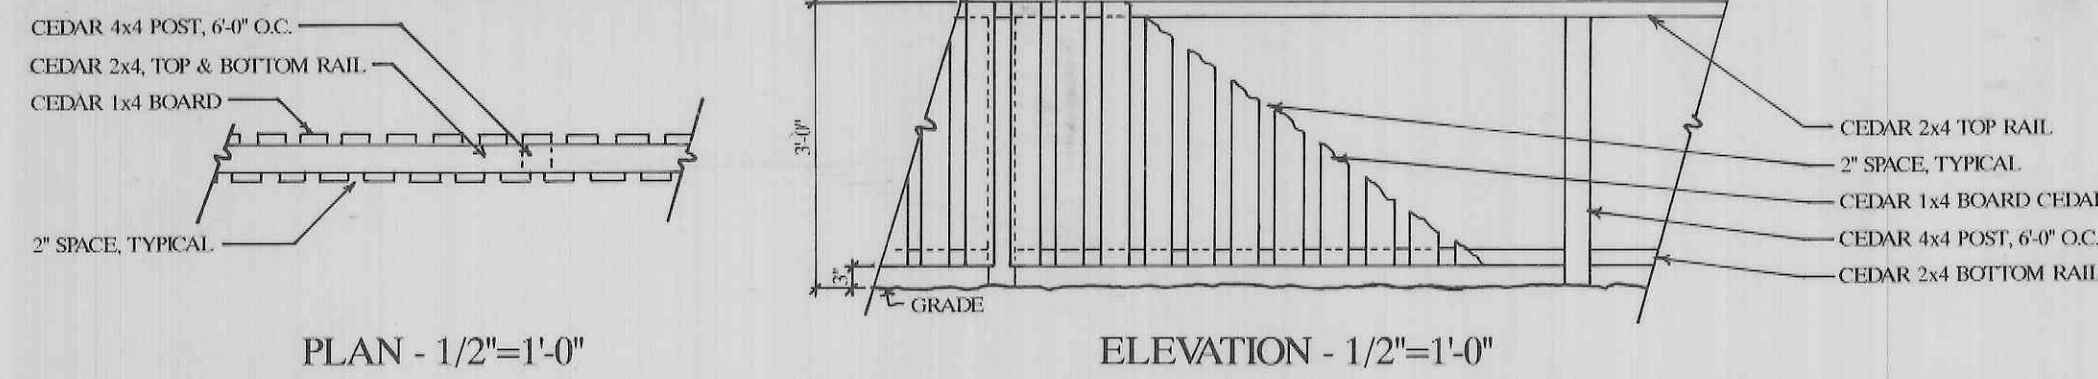

PLAN - 1/2"=1'-0"

ELEVATION - 1/2"=1'-0"

P.U.D. LIMIT

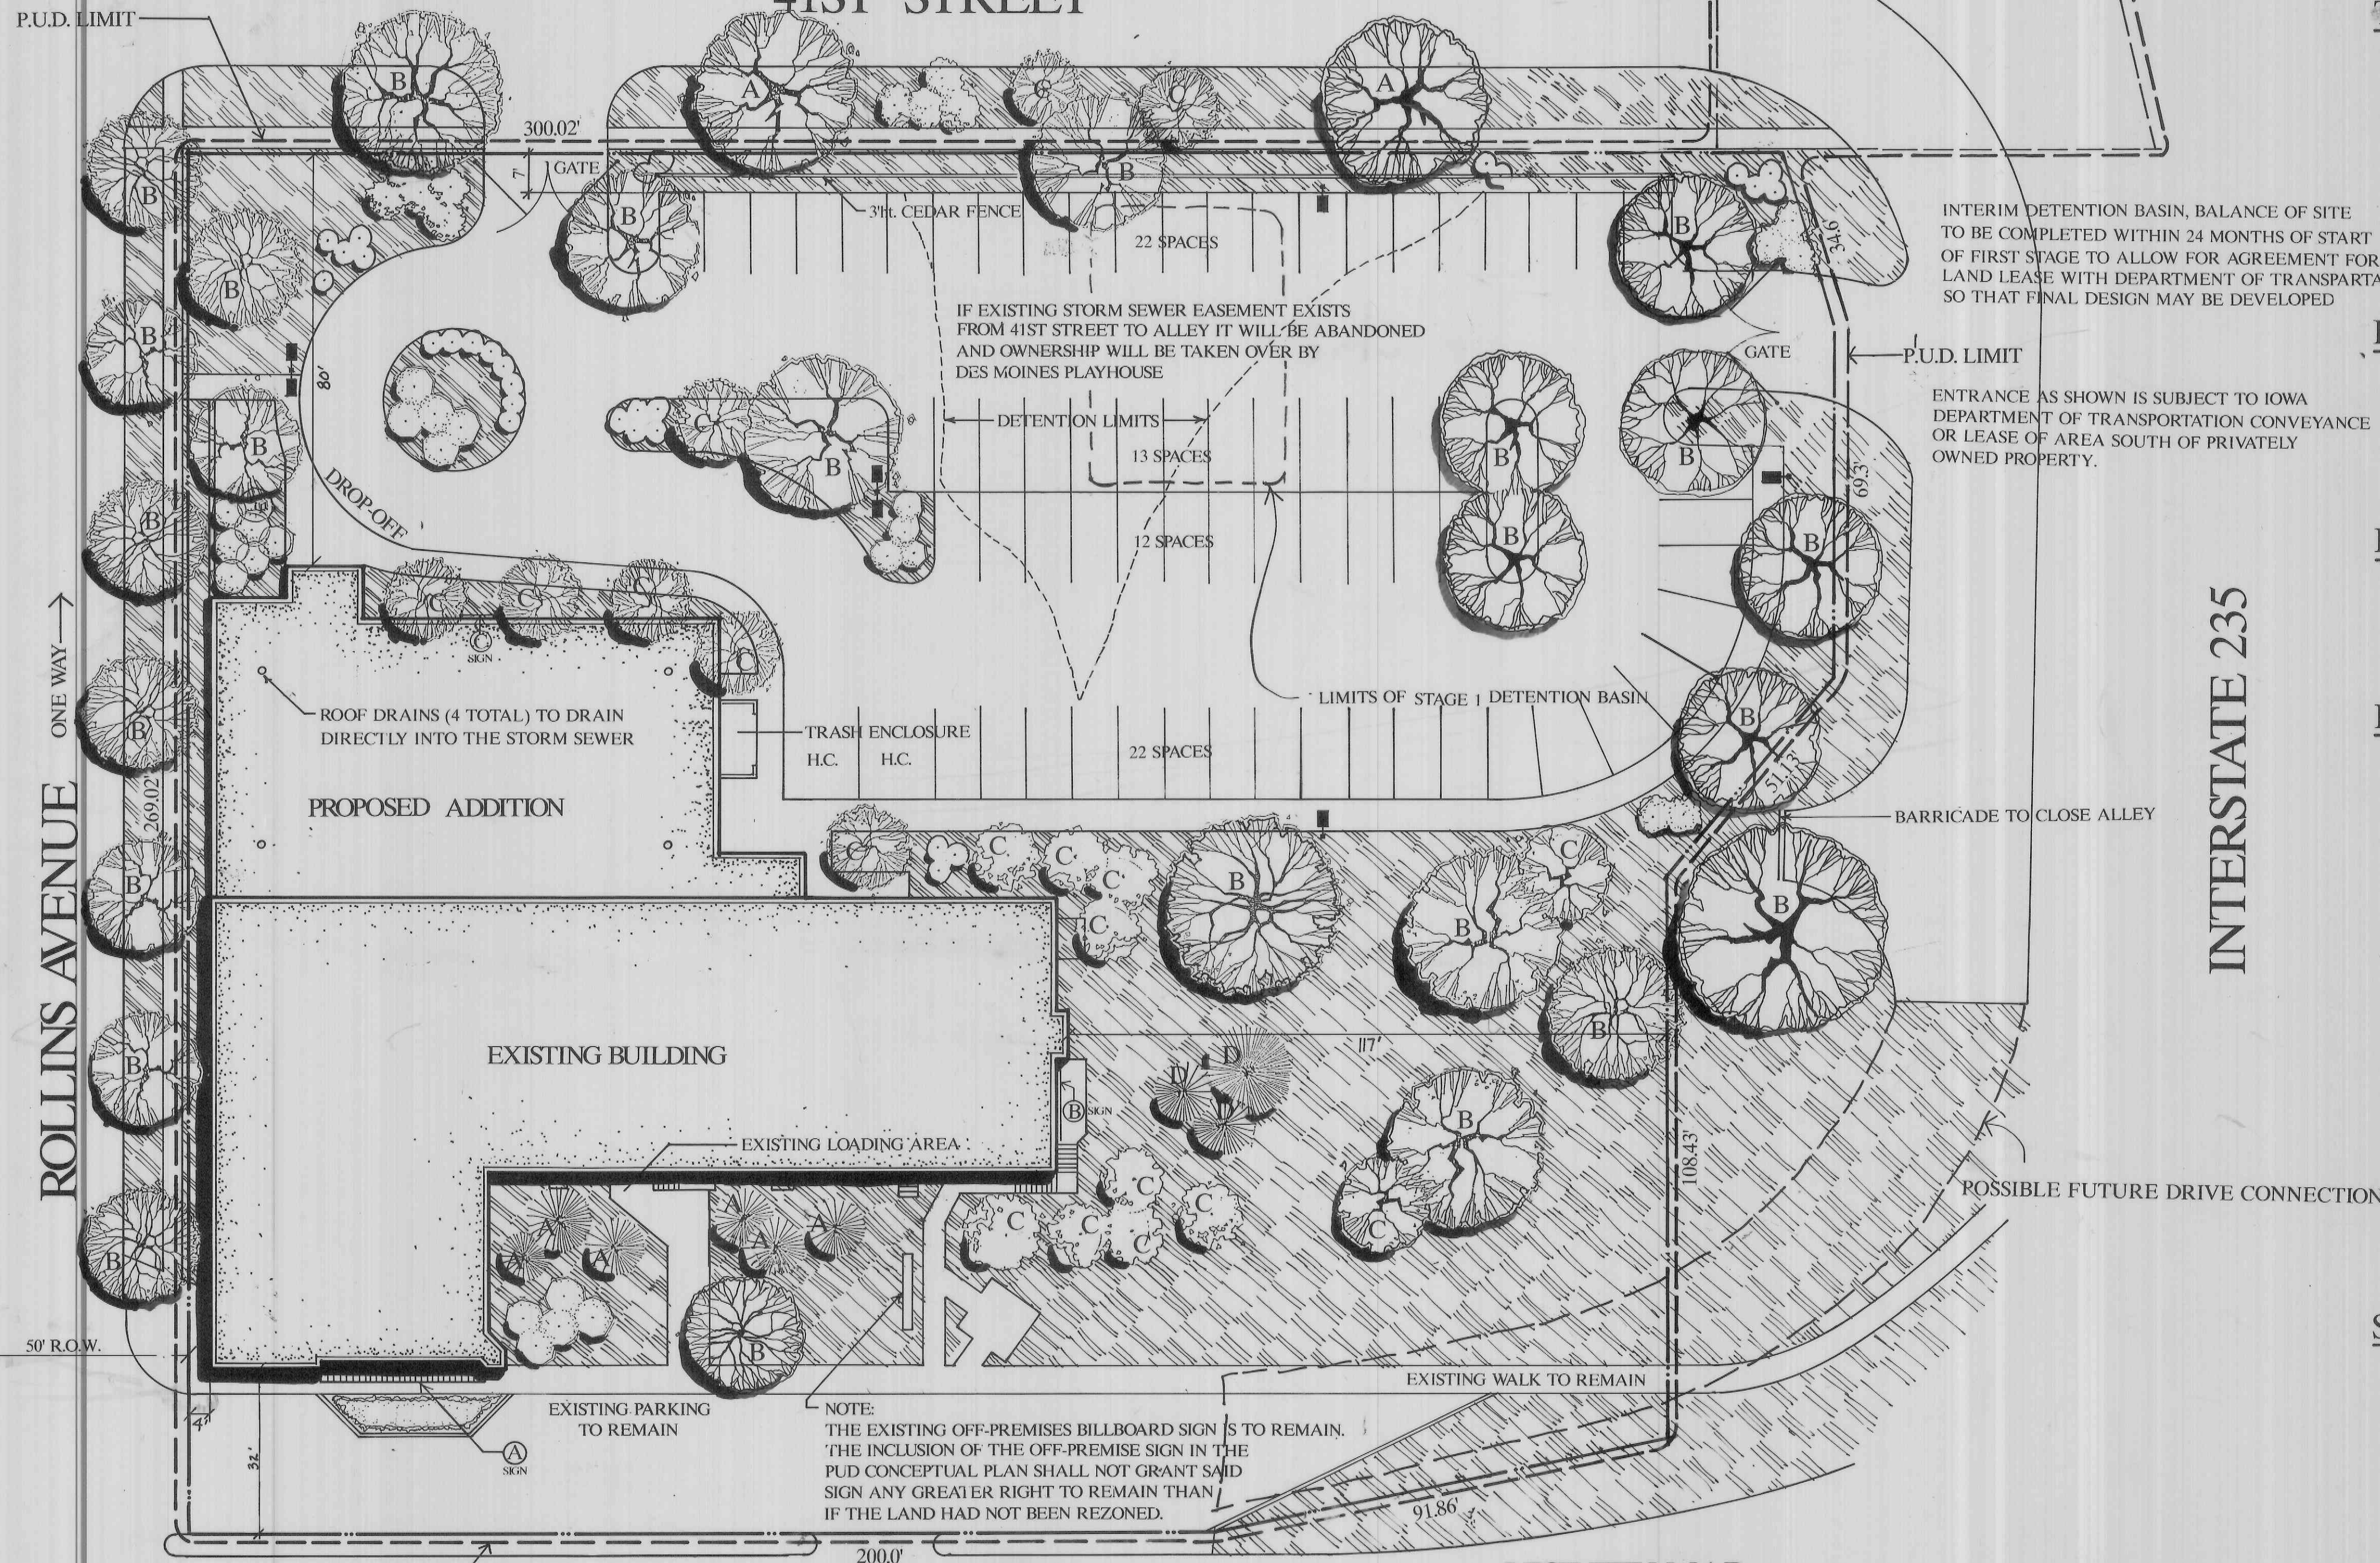

BUILDING SQUARE FOOTAGE

EXISTING - 20,523 S.F.
PROPOSED - 11,960 S.F.
EXISTING BUILDING - 2 STORY
PROPOSED - 2 STORY

THEATER SEATING

EXISTING SEATS:
MAIN THEATER: 426 SEATS
LOWER THEATER: 98 SEATS
TOTAL: 524 SEATS

PROPOSED SEATS:
MAIN THEATER: 426 SEATS
NON FIXED SEATING IN NEW CHILDREN'S THEATER: 250 SEATS MAX.
TOTAL: 676 SEATS

PARKING

EXISTING - 15 SPACES
PROPOSED - 69 SPACES

P.U.D. / SITE ACREAGE


TOTAL - 2.065 ACRES

PARKING LOT LIGHTING

- TWIN HEAD 400 WATT HIGH PRESSURE SODIUM
- SINGLE HEAD 400 WATT HIGH PRESSURE SODIUM



BREAKAWAY GATE DETAIL

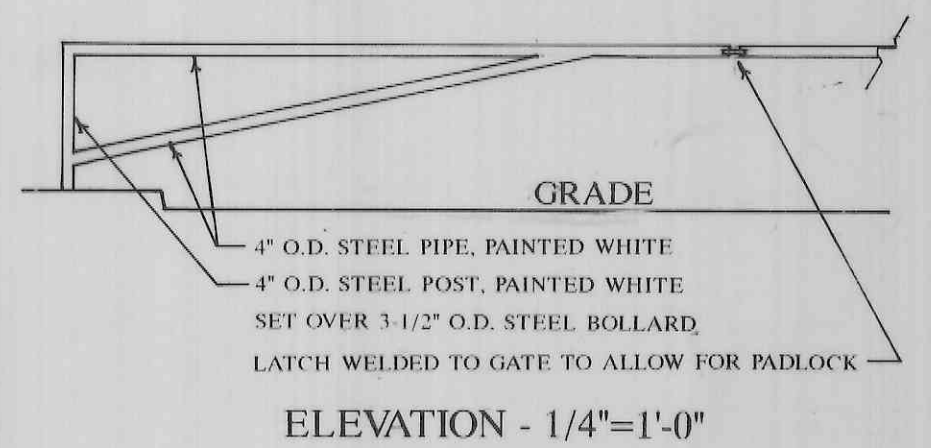

GATES WILL BE PROVIDED AT PARKING LOT ENTRANCES SO LOT CAN BE CLOSED AT OFF HOURS. GATES ARE TO BE BREAKAWAY TYPE FOR EMERGENCY VEHICLE ACCESS.

SIGNAGE

- (A) WALL SIGN INTERNALLY LIGHTED (36 S.F.)
- (B) WALL SIGN INTERNALLY LIGHTED (36 S.F.)
- (C) WALL SIGN NON-LIGHTED (32 S.F.)


ZONING

P.U.D.


BUILDING SCHEDULE

START PROJECT WITHIN 1 MONTH OF THE PLANNING DIRECTOR'S APPROVAL AND COMPLETE WITHIN 10 MONTHS

DES MOINES PLAYHOUSE
831 42ND STREET
DES MOINES, IA 50312
(515) 277-6261

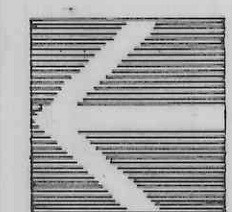

DATE: FEBRUARY 24, 1994
REVISED: MARCH 28, 1994
APRIL 26, 1994

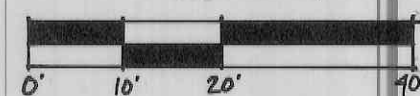

ENVIRONMENTAL DESIGN GROUP, LTD.
ARCHITECTS • LANDSCAPE ARCHITECTS • PLANNERS
4090 Veterans Parkway Suite E West Des Moines, Iowa 50344 (515) 224-0022

THE PORTION OF THE TECHNICAL SUBMISSION DESCRIBED BELOW HAS BEEN PREPARED UNDER THE DIRECT SUPERVISION AND RESPONSIBLE CHARGE OF THE UNDERSIGNED.

SIGNATURE: *Dennis A. Hansen*

DISCIPLINE: LANDSCAPE ARCHITECT

IOWA REGISTRATION NO. 230

PAGES OR SHEETS COVERED BY THIS SEAL: SP-1

DATE OF ISSUANCE: 3/28/94



ADJACENT LAND USE DESCRIPTION

- WEST - EXISTING BRICK STRUCTURE ROOSEVELT HIGH SCHOOL
- NORTH - EXISTING MASONRY STRUCTURE CONTAINING ROOSEVELT SHOPPING ON WEST END OF ROLLINS AVENUE, EXISTING OPEN PARKING LOT ON EAST SIDE OF ROLLINS AVENUE ACROSS 41ST STREET - EXISTING WOOD FRAME SINGLE-FAMILY RESIDENCES
- EAST - INTERSTATE 235 WITH EXISTING WOOD FRAME SINGLE-FAMILY RESIDENCES AND BRICK BUILDING OWNED BY DES MOINES FIRE DEPARTMENT SOUTH OF THE INTERSTATE


APPROVED BY COMMISSION:

APPROVED BY COUNCIL:

PUD ZONING APPROVED BY COUNCIL:

4/17/94
DATE
6/20/94
DATE
94-2320
ROLL CALL NO.
6/20/94
DATE
94-2321
ROLL CALL NO.
13,049
ORDINANCE NO.

VICINITY MAP

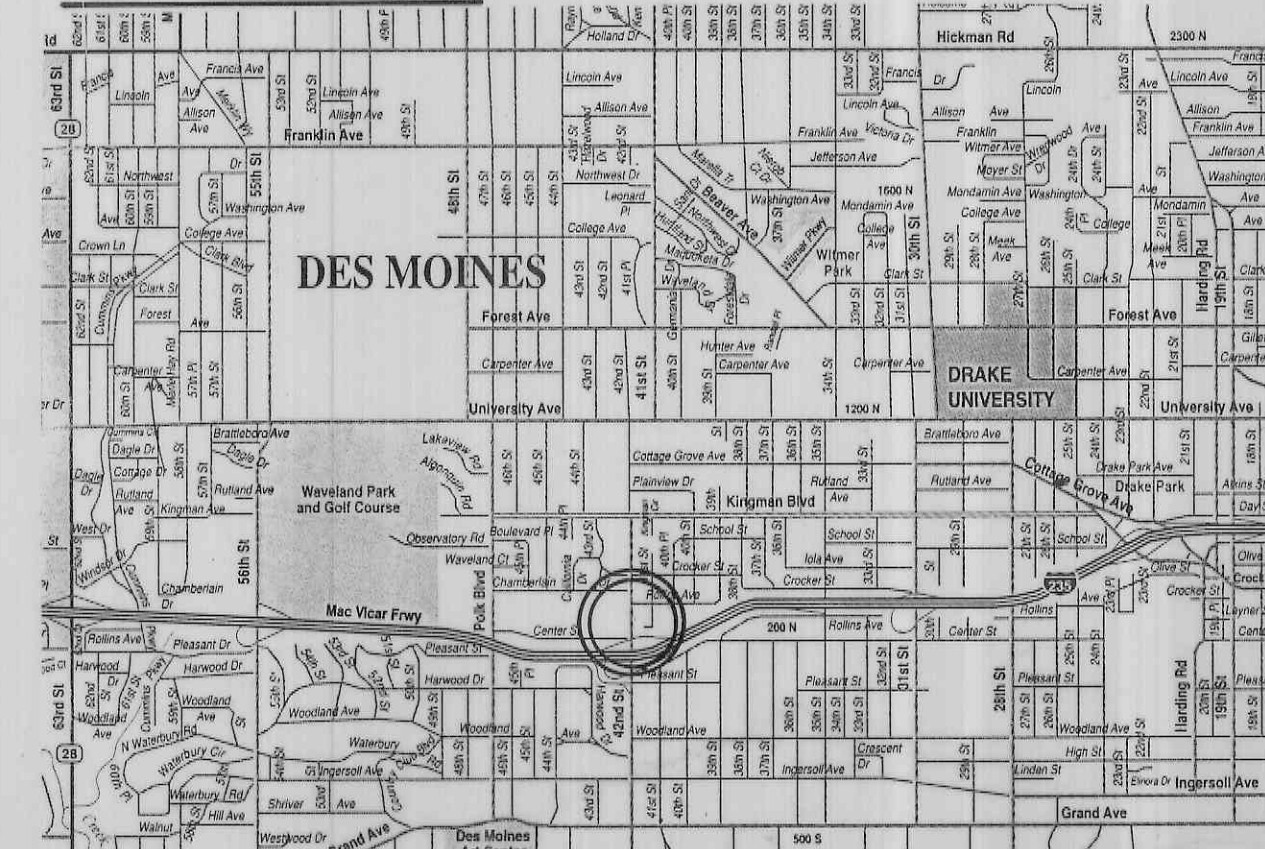

DES MOINES PLAYHOUSE
P.U.D. CONCEPTUAL MASTER PLAN

10-94-1.03